
REVISION HISTORY

S.No	Revision	Date	Description	Remarks	Checked By	Approved By
1	Rev 00	11/09/2026	Initial Release	-	Manju. M	Vengatesh. A


SCHNELL ENERGY EQUIPMENTS PVT LTD	
PROJECT TITLE: SILM MIOTY - RF	
SHEET NAME: REVISION HISTORY	
DATE: 21-09-2026	REVISION: 00
DRAWN BY: MANJU. M	SHEET NO: 1/4
APPROVED BY: VENGATESH. A	SCALE: NTS

BLOCK DIAGRAM - SILM MIOTY RF MODULE

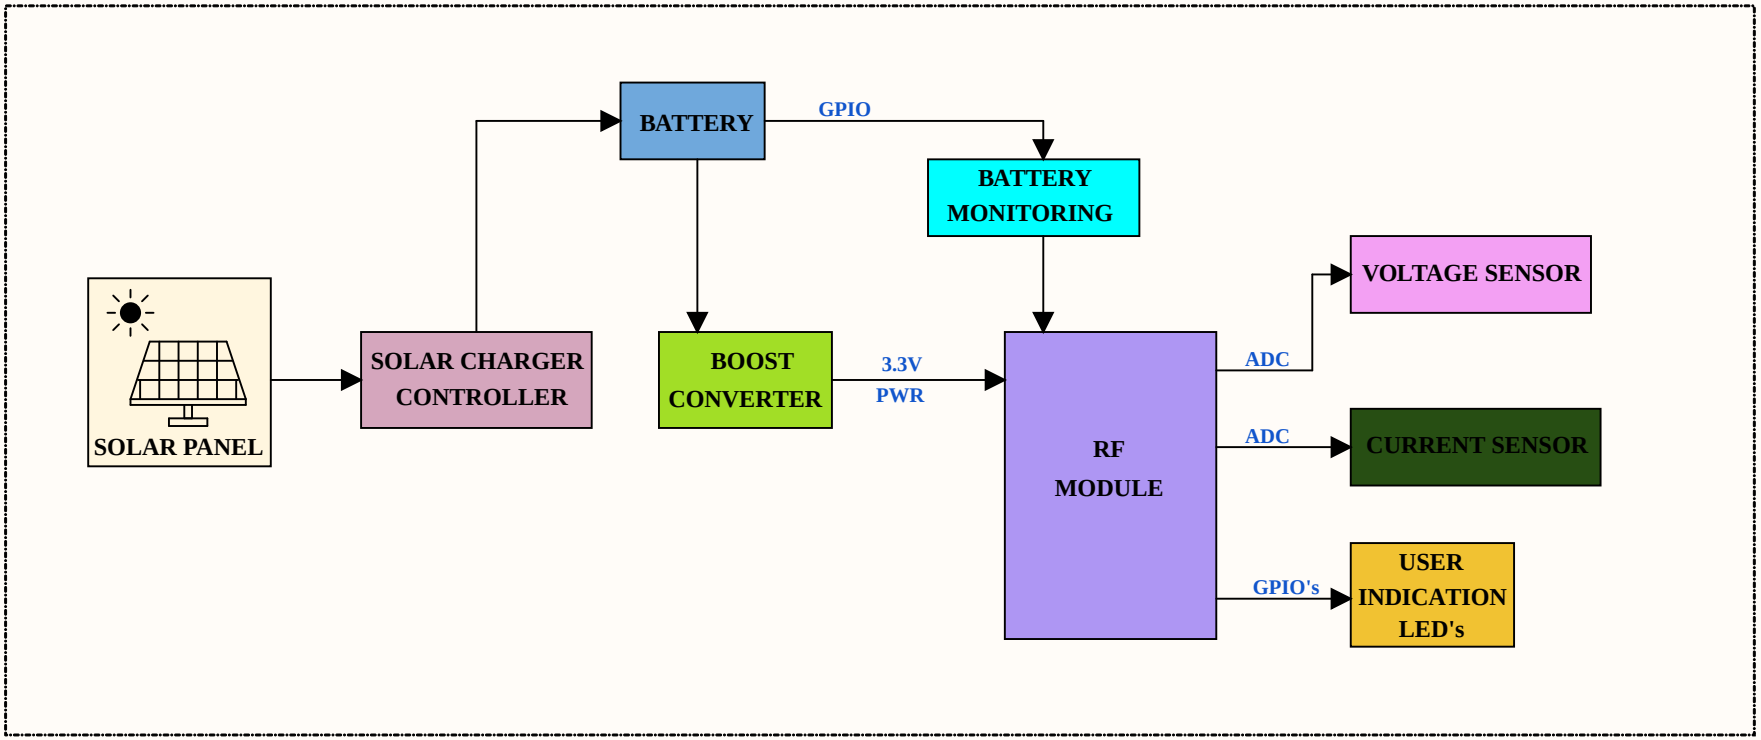


SCHNELL ENERGY EQUIPMENTS PVT LTD	
PROJECT TITLE: SILM MIOTY - RF	
SHEET NAME: BLOCK DIAGRAM	
DATE: 21-09-2026	REVISION: 00
DRAWN BY: MANJU. M	SHEET NO: 2/4
APPROVED BY: VENGATESH. A	SCALE: NTS


SOLAR CHARGER SECTION

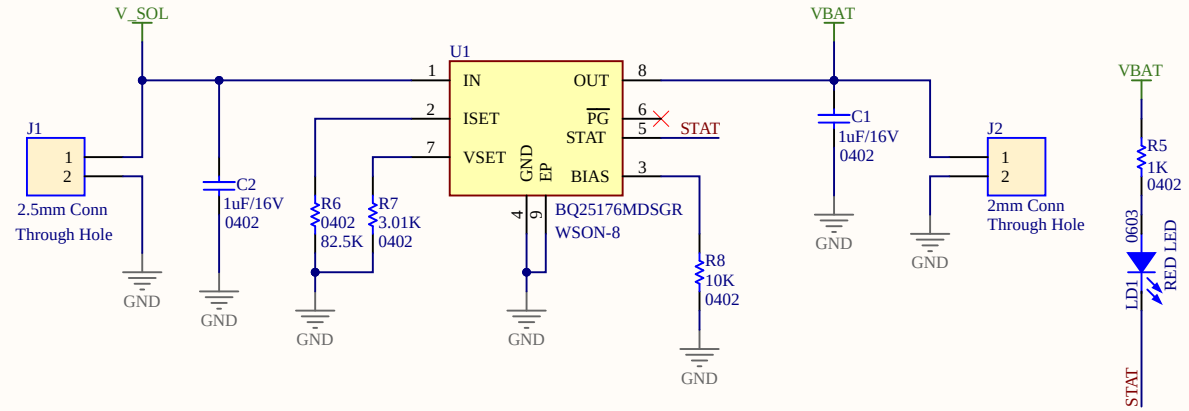


HALL EFFECT SENSOR SECTION

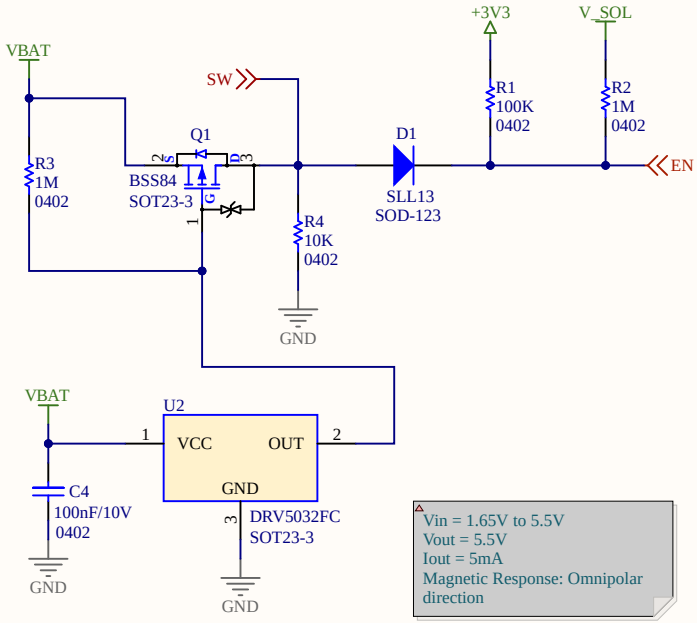


BOOST CONVERTER SECTION

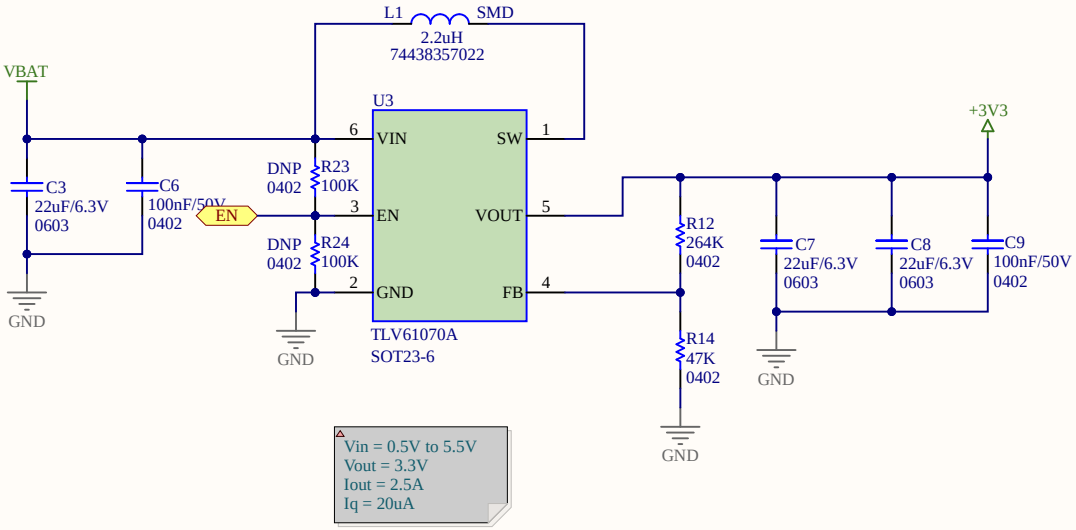

SOLAR POWER SENSE SECTION

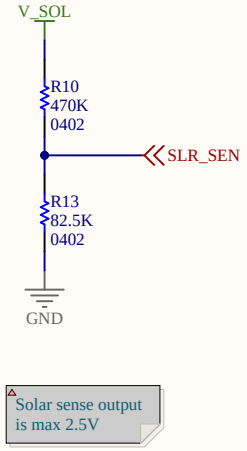


BATTERY MONIOTRING SECTION

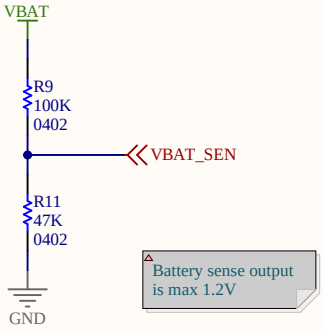


SCHNELL ENERGY EQUIPMENTS PVT LTD	
PROJECT TITLE: SILM MIOTY - RF	
SHEET NAME: POWER SUPPLY & CHARGER SECTION	
DATE: 21-09-2026	**REVISION:** 00
DRAWN BY: MANJU. M	**SHEET NO:** 3/4
APPROVED BY: VENGATESH. A	**SCALE:** NTS


VOLTAGE SENSOR SECTION

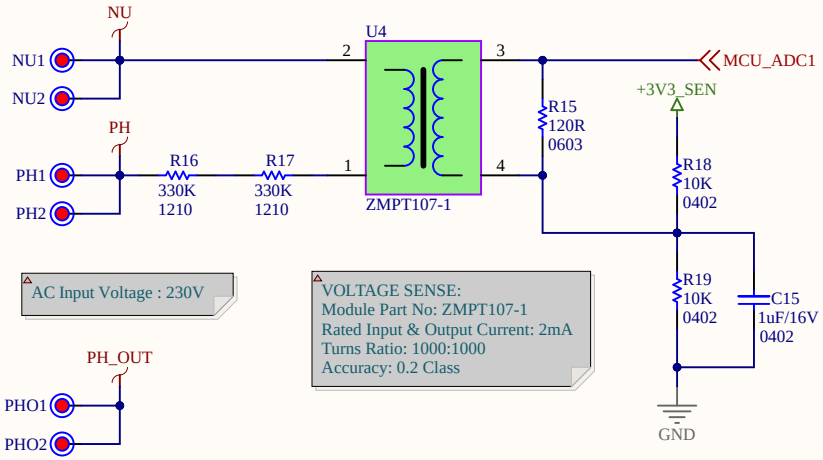


RF MODULE SECTION

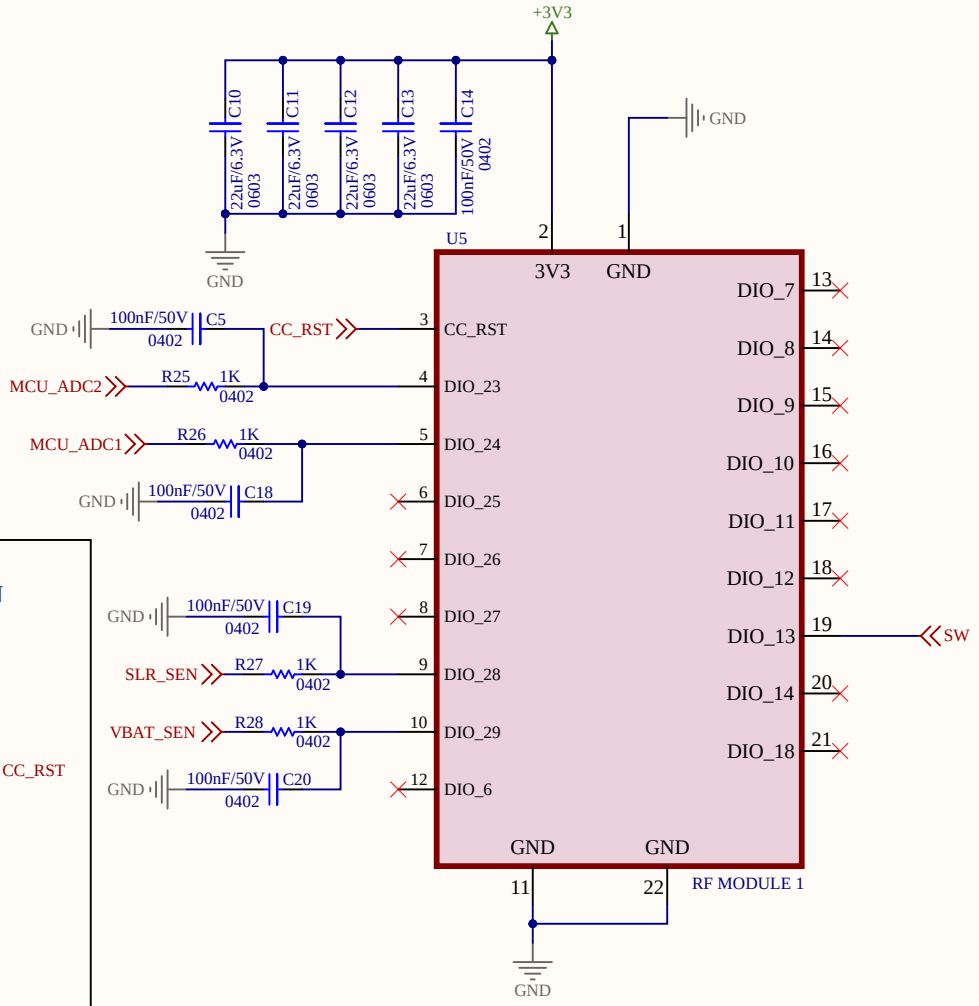

CURRENT SENSOR SECTION

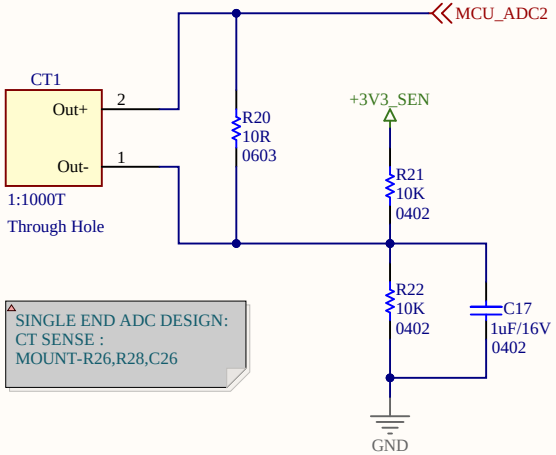

VOLTAGE SUPERVISOR SECTION

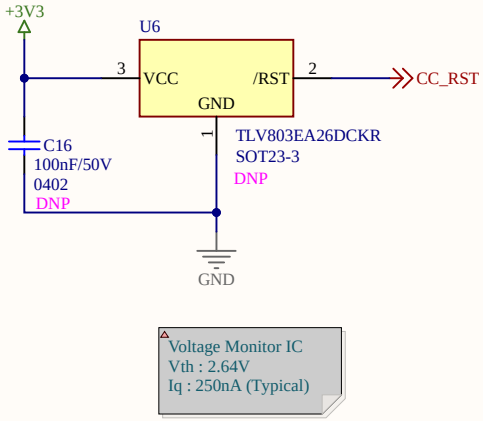

SCHNELL ENERGY EQUIPMENTS PVT LTD	
PROJECT TITLE: SILM MIOTY - RF	
SHEET NAME: RF MODULE SECTION	
DATE: 21-09-2026	REVISION: 00
DRAWN BY: MANJU. M	SHEET NO: 4/4
APPROVED BY: VENGATESH. A	SCALE: NTS